A frontage rebuilt from the plans

West-facing house. Terracotta roof, ivory walls and green joinery; privacy developed around the retained opening positions.



Entrance in the return

The 1.10 m entrance sits in the north-facing return at the right end of the 3.13 x 1.50 m verandah.

Windows and bays retained

Two separate kids' front windows; living corner window; projecting master, kids' north and upper bedroom bays.

Roof falls toward west

The central single-pitch roof slopes down toward the front. The front upper void stays open above the living room.

Privacy at the road

Opaque lower window panels, a shaded verandah and a proposed boundary screen work with the approximately 4 m forecourt.

Drawing basis: sheets 09, 10, 11 and 12 supplied by you. Horizontal wall and opening locations are traced from the PDF vectors and calibrated to the printed 12.84 m width. Heights, framing, roof design and finishes are proposals.

West elevation + opening alignment

Facing the house: north is left, south is right. A strict west view sees the main entrance edge-on because it is in the return wall.



G01 + G02

Two narrow kids' windows separated by the solid bed-head wall.

G04 + G05

One living corner window, wrapping from west to north.

G06

Master bedroom bay projects 0.70 m as dimensioned.


F01

Upper bedroom bay: 2.00 m clear width, 0.60 m projection.

D01

1.10 m main door on the return. See sheet 03.


GROUND-FLOOR FRONT TRACE

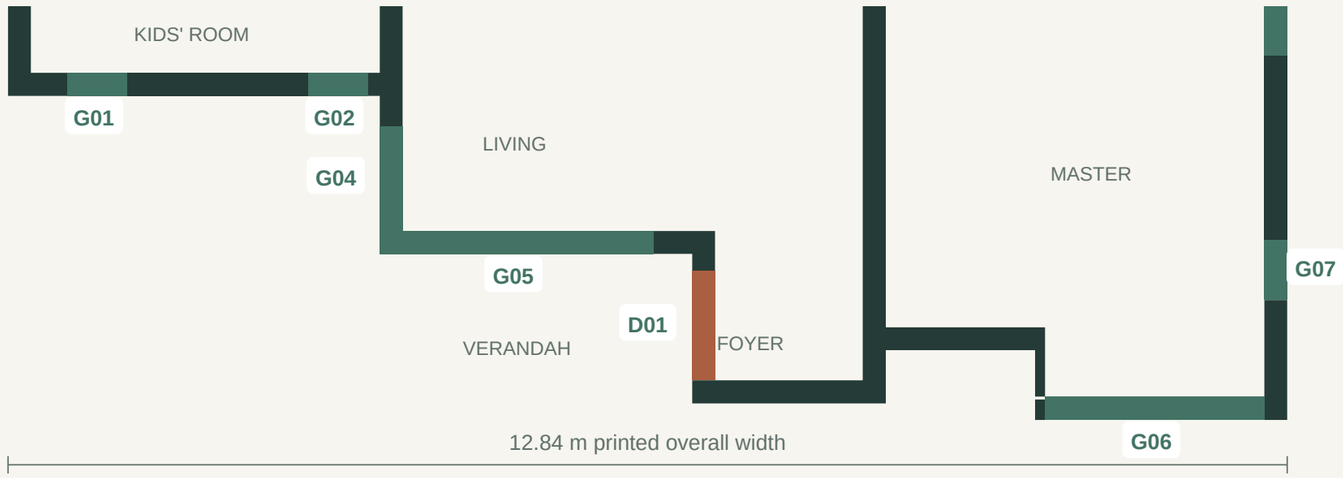


Green = window opening. Terracotta = door opening. This trace records positions; use the source plan for the full internal layout. Unscheduled widths are graphic-derived.

The entrance is on the side return

D01 is not a door in the rear wall of the verandah. It is the 110 cm opening at the verandah's right end and opens inward into the foyer.

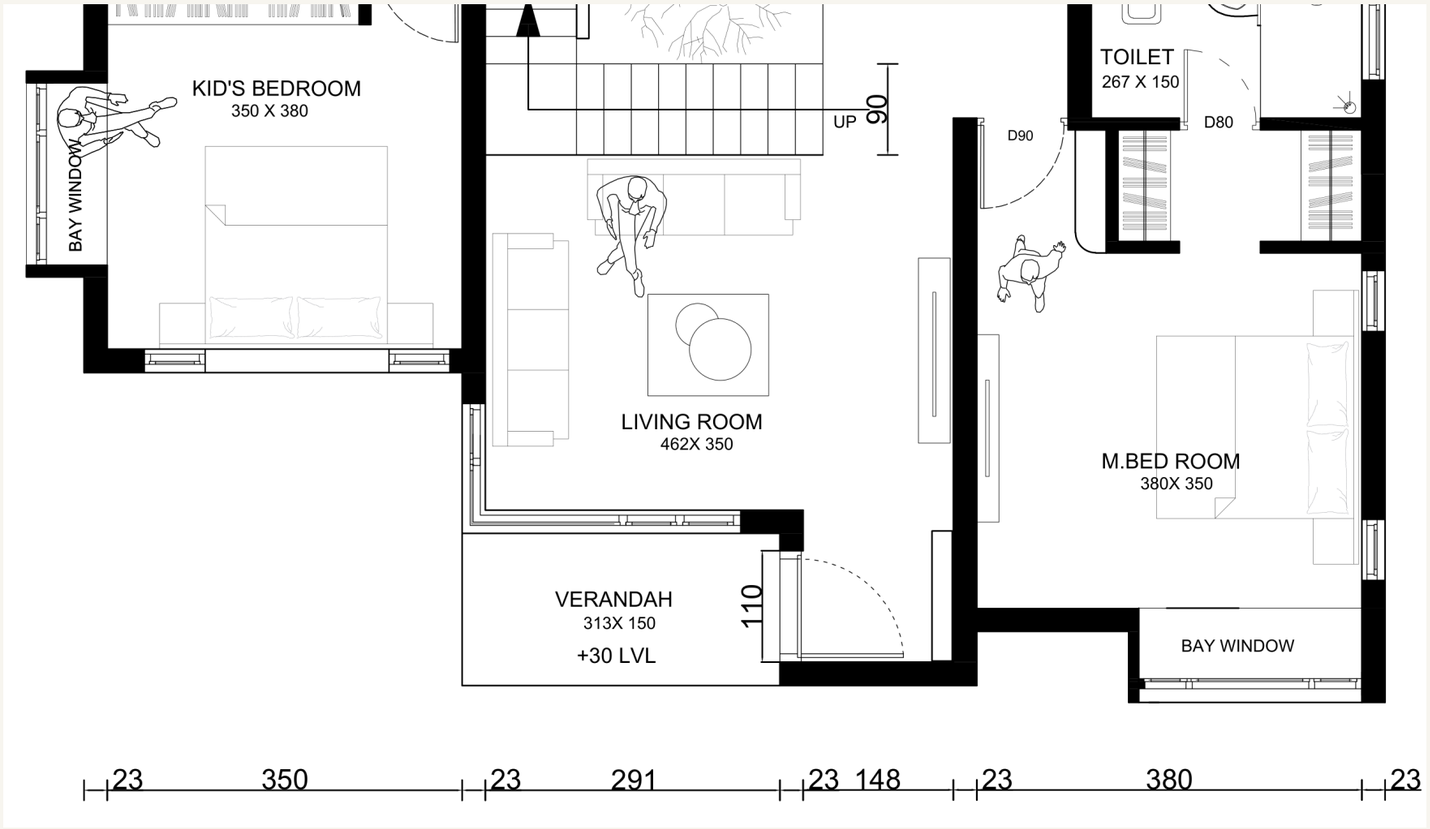

SOURCE: SHEET 11 / FRONT ROOMS AND ENTRY

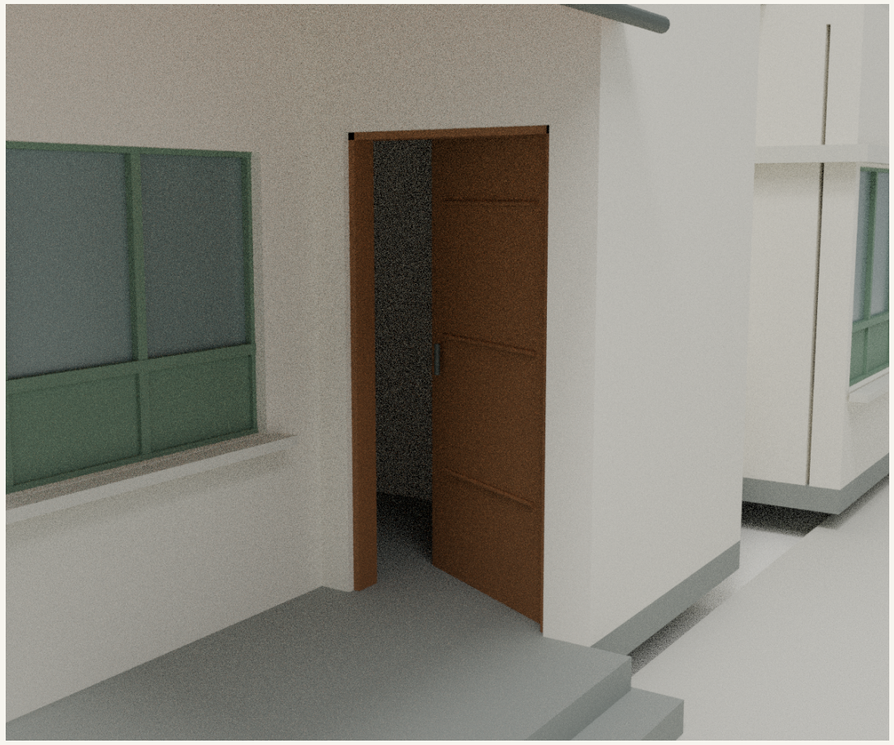

MODEL: LOOKING TOWARD THE NORTH-FACING RETURN

Verandah: 3.13 x 1.50 m, with +30 cm level printed on the plan.

Main entrance: 1.10 m clear opening; source jamb position retained.

Living room: 4.62 x 3.50 m; its west window turns around the north corner.

Master bay and bedroom side windows remain separate from the entrance.

Proposed treatment: a timber door, a small tiled canopy and one slim outer support. The render shows the door partly open to make its location visible. Door height, sill/head levels, canopy structure and approach-step detailing remain to be designed.


North and south elevations

The side windows, bay projection and terrace access have been retained. Views use the same source-traced model as the west elevation.



NORTH / rear at left, front at right

G15 parents' bedroom, G16 bathroom ventilator, G03 kids' projecting bay, G04 living corner return and D01 main entrance. F02 is the upper bedroom window.

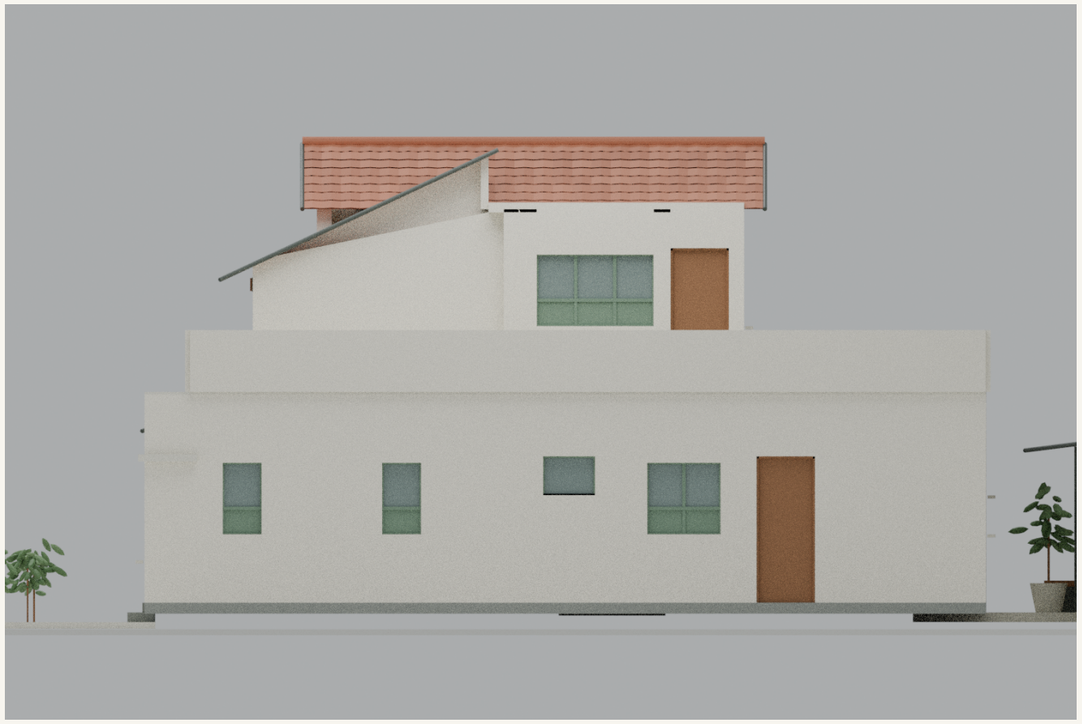

SOUTH / front at left, rear at right

G07 and G08 remain two narrow master-bedroom windows. G09 bathroom, G10 work-area window and D02 external door are retained. F04 and D03 serve the upper landing and terrace.

WHY THESE VIEWS MATTER

The west view alone hides the main door and the kids' north bay. Together, the front, side and oblique drawings show the setbacks and projections that were missing from the earlier images.

Proposed window divisions and opaque lower panels are an elevation treatment; horizontal opening positions follow the plan. The model is a massing study and does not detail foundations, reinforcement or roof junctions.

Roof direction + double-height living

Central roof: high to the east, low to the west. The upper front void and gallery remain in their plan positions.



Front void

The upper plan marks 2.20 m depth as SEEN BELOW; the gallery behind it is 1.20 m deep.

Internal courtyard

The 2.43 x 1.80 m stair courtyard remains open through the roof. It is separate from the rear courtyard.


Open terrace

The south and rear terrace remain accessible. The back slab outline is provisional where the NTS upper plan lacks dimensions.

Construction economy

A steel-and-tile roof over the living void is a candidate alternative to RCC there. Retained terraces still need their slabs; cost savings require a local comparison.

SCHEMATIC EAST-WEST SECTION THROUGH CENTRAL LIVING / GALLERY

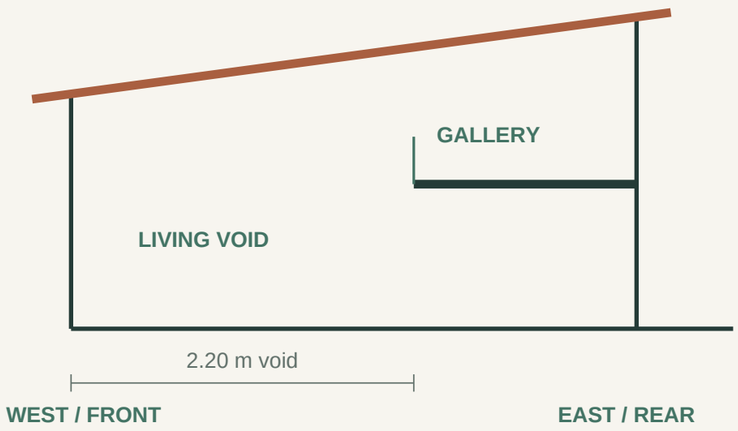


Section is diagrammatic, not to scale. Proposed levels above ground-floor finish: upper floor +3.20 m; central roof about +5.20 m at its front bearing and +6.90 m at its rear bearing. Proposed pitch: 25 degrees, subject to tile specification and drainage design.


Use exposed dark steel and terracotta tile undersides as in your references, with a coordinated weatherproof and thermal build-up. Keep west glazing shaded and use a small screened high-level vent. Structural spans, connections, gutters and wind restraint need design.

Rear courtyard: 3.30 x 2.63 m

The 2.63 m dimension runs from the dining-room outer face to the compound wall. The dining opening shown in the plan remains a window.

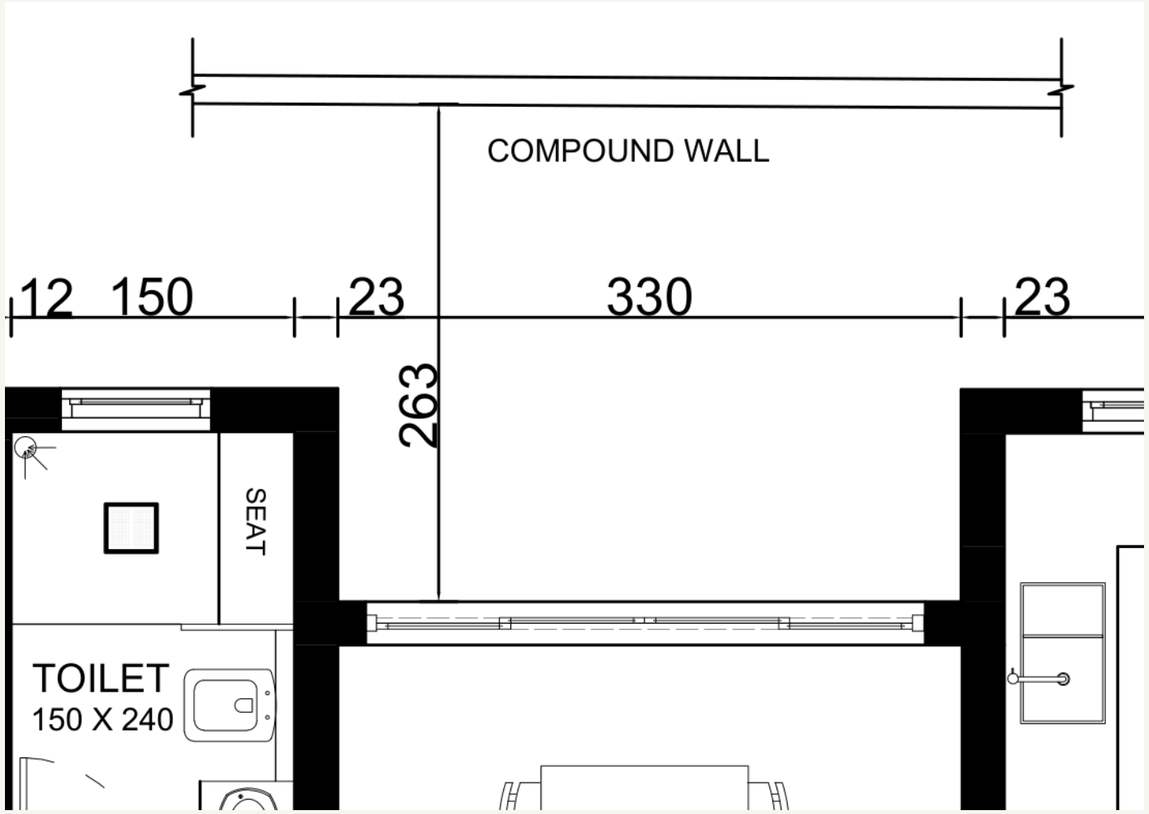

SOURCE: SHEET 11 / REAR DIMENSION

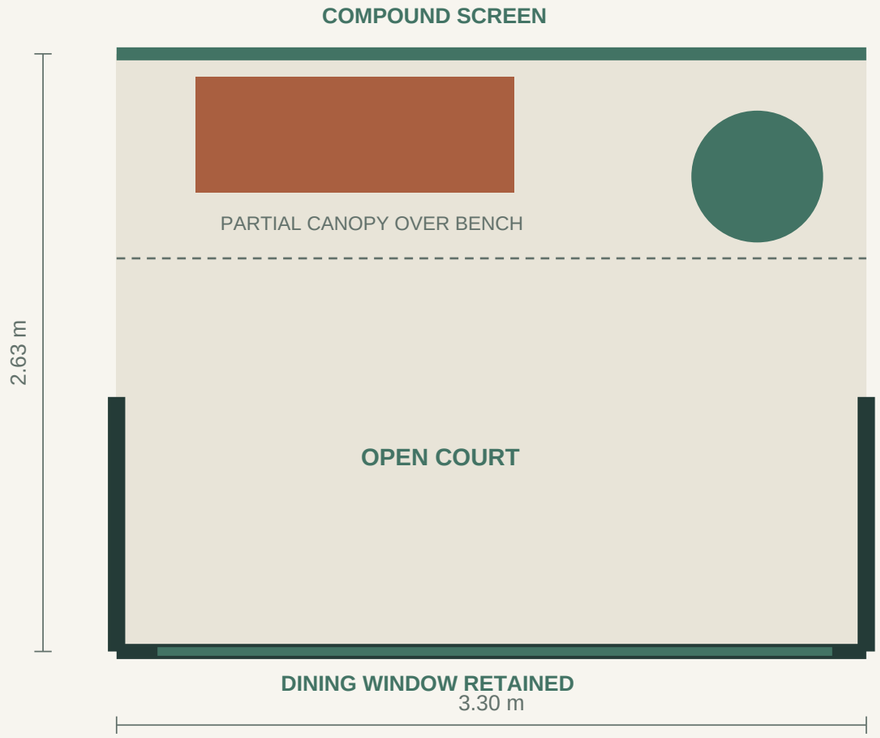

PROPOSED COURTYARD PLAN


Reference translated to the actual plan: a compact fixed timber bench, one potted tree, a screened rear boundary and a partial canopy above the bench. The fixed bench keeps the shallow court usable without a swing's travel zone.

The building recess is approximately 1.12 m deep; the court continues behind the flanking wings to the compound wall. Keep the lateral access routes clear. No new dining-room door or full glazed opening has been added.

Court floor level, falls and drain location are proposals to coordinate with the house plinth and the site. The reference screenshot does not establish a construction level.

Privacy toward the public road

Approximately 4.00 m from verandah front to road-side compound wall, as you confirmed. Boundary position and heights require a site check.

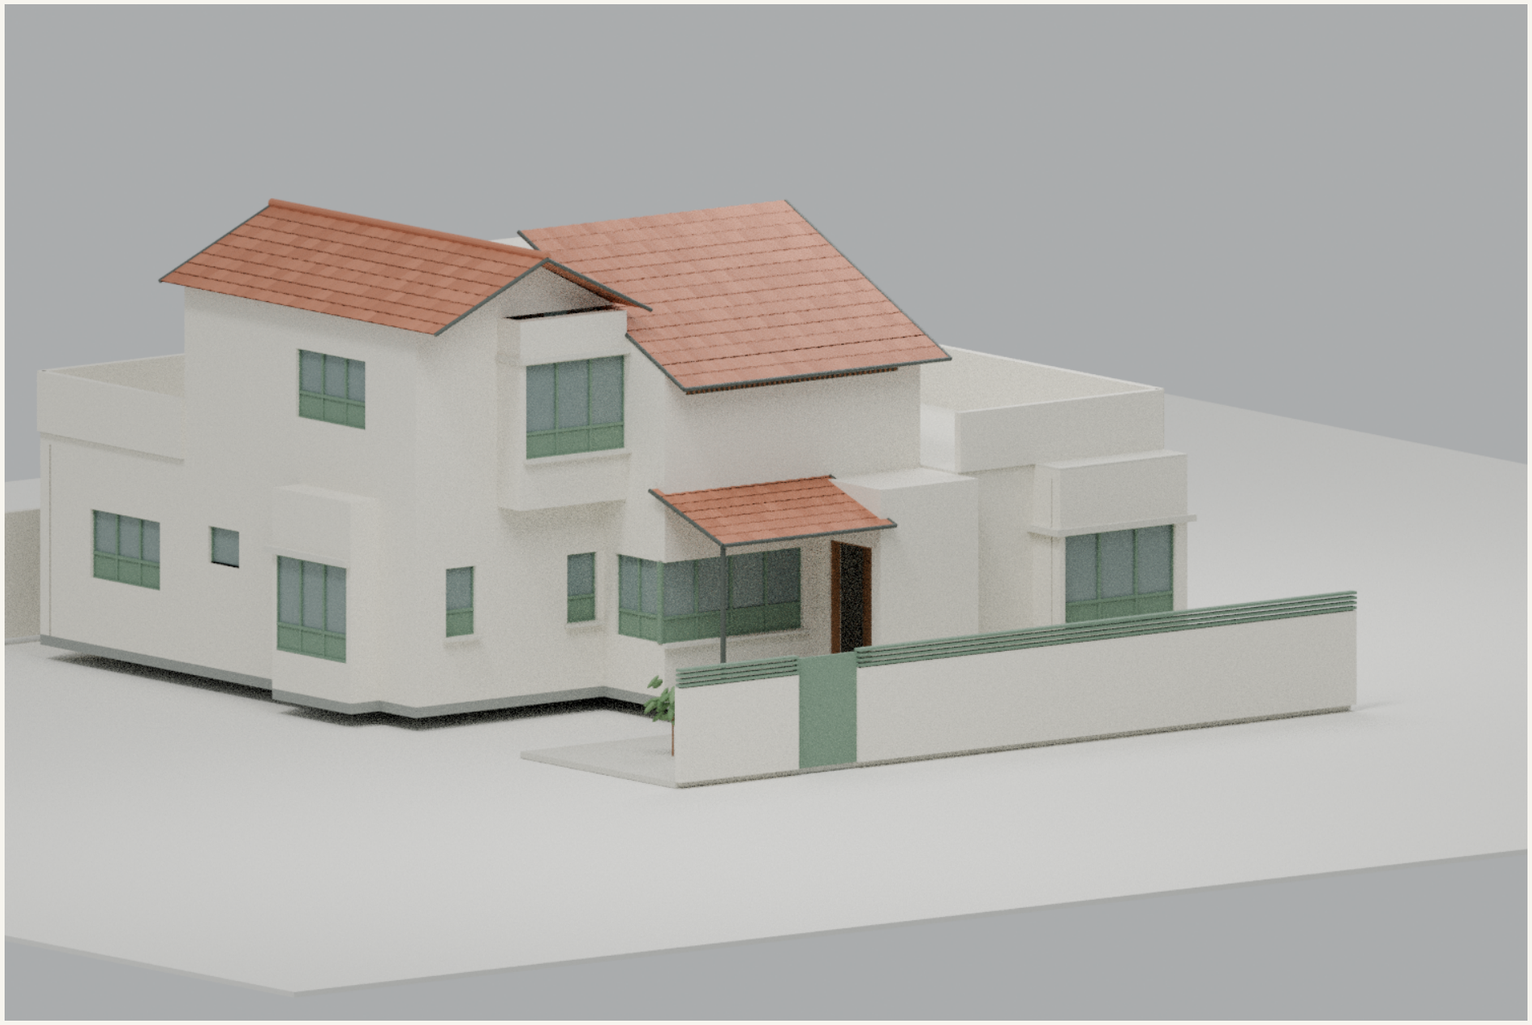

Screen the boundary

Proposed 1.50 m solid base plus about 0.30 m louvred top. Set blade angles after checking road levels and sightlines.

Offset the pedestrian gate

The proposed gate sits away from a straight view into the entrance. Keep the approach unobstructed.

Reduce exposed glazing

Retain plan openings but use opaque lower joinery panels, shaded upper glass and internal curtains/shutters.

Retain west sun protection

The verandah canopy and deep roof edge provide shade. Avoid an unshaded double-height glass facade.

This is an elevated context view so the house remains visible above the boundary; it does not simulate a pedestrian's exact sightline. A 1.80 m screen can improve privacy, but its effectiveness depends on the public-road level, gate position and viewing height.

Vehicle access and parking have not been inferred from the building plans. The shown boundary is a privacy concept to coordinate with the surveyed plot, access needs and local wall-height requirements.

Opening register + source checks

IDs link the plan trace, model and review notes. Widths marked ~ are graphic-derived from NTS plans, not a construction opening schedule.

ID	LEVEL / FACE	OPENING	WIDTH
G01	GF / W	Kids bedroom front window - left	~ 0.60 m
G02	GF / W	Kids bedroom front window - right	~ 0.60 m
G03	GF / N	Kids bedroom north-facing bay	~ 1.80 m
G04	GF / N	Living corner window - north return	~ 1.05 m
G05	GF / W	Living corner window - west face	~ 2.75 m
G06	GF / W	Master bedroom projecting front bay	~ 2.20 m
G07	GF / S	Master bedroom south window - front	~ 0.60 m
G08	GF / S	Master bedroom south window - rear	~ 0.60 m
G09	GF / S	Master bathroom ventilator	~ 0.80 m
G10	GF / S	Work-area window	~ 1.13 m
G11	GF / E	Kitchen rear window	~ 2.70 m
G12	GF / E	Dining window toward rear court - not a doorway	~ 2.97 m
G13	GF / E	Parents bathroom rear ventilator	~ 0.80 m
G14	GF / E	Parents bedroom rear window	~ 1.80 m
G15	GF / N	Parents bedroom north window	~ 1.80 m
G16	GF / N	Shared bathroom north ventilator	~ 0.80 m
F01	FF / W	Upper bedroom projecting front bay	2.00 m
F02	FF / N	Upper bedroom north window	~ 1.80 m
F03	FF / E	Upper landing rear window	~ 2.70 m
F04	FF / S	Upper landing south window	~ 1.80 m
D01	GF / N	Main entrance, 110 cm, opens inward into foyer	1.10 m
D02	GF / S	Kitchen/work-area external door, 90 cm	0.90 m
D03	FF / S	Upper landing door to open terrace, 90 cm	0.90 m

CHECKS COMPLETED

20 exterior window groups and 3 exterior doors recorded.

D01 is in the north-facing return, with 1.10 m width.

G01 / G02 are separate. G04 / G05 meet at the living corner.

Front upper slab does not cover the living void.

Internal courtyard stays open through the stair roof.

Rear court follows 3.30 x 2.63 m to the compound wall.

Printed dimensions take precedence over graphic measurements. The 4.92 m upper dimension is at the rear landing; the right wall steps inward toward the approximately 4.62 m front living span. These are different locations, not a demonstrated plan conflict.

Design basis + items still to resolve

This revision is a source-based elevation concept for review. It is not a permit, structural design or construction drawing set.

RETAINED FROM YOUR PLANS

Ground-floor footprint and the staggered front walls; verandah, foyer and room relationships.

Exterior window and door locations, including the side-facing entrance, corner glazing and all recorded bays.

Upper bedroom, landing, 2.20 m front void and 1.20 m gallery.

Internal 2.43 x 1.80 m courtyard and rear 3.30 x 2.63 m courtyard.

PROPOSED IN THIS STUDY

All storey heights, opening heights, roof levels and roof pitch; no section or height schedule was supplied.

Ivory plaster, green joinery, timber door, terracotta roof and opaque lower window panels.

Steel-and-tile roof construction concept; verandah canopy and support; soffit vent and parapet design.

Road-side screen, offset gate and landscape; rear bench, screen and partial canopy.

NEEDS DIMENSIONAL / SITE DESIGN

The undimensioned rear terrace outline differs graphically between floors. This model limits its slab to the supporting ground-floor footprint pending confirmation.

Surveyed site levels, compound-wall location, road level, vehicle access and drainage.

Window schedule, detailed door swing/clearances, roof junctions, waterproofing, thermal build-up and rainwater disposal.

Structural support and reinforcement, roof framing and wind restraint; itemised local cost comparison.

Sources reviewed: 09 - AREA GROUND FLOOR; 10 - AREA FIRST FLOOR; 11 - DETAILED PLAN GROUND FLOOR; 12 - DETAILED PLAN FIRST FLOOR. Your reference images inform the roof/material palette and courtyard atmosphere; the supplied plans govern horizontal geometry.

Drawing method: PDF vector tracing, explicit opening register and a single Blender model. No AI-generated illustration is used as evidence of dimensional alignment. Render shadows and surface noise are visualisation artefacts; foundations and services are not detailed.